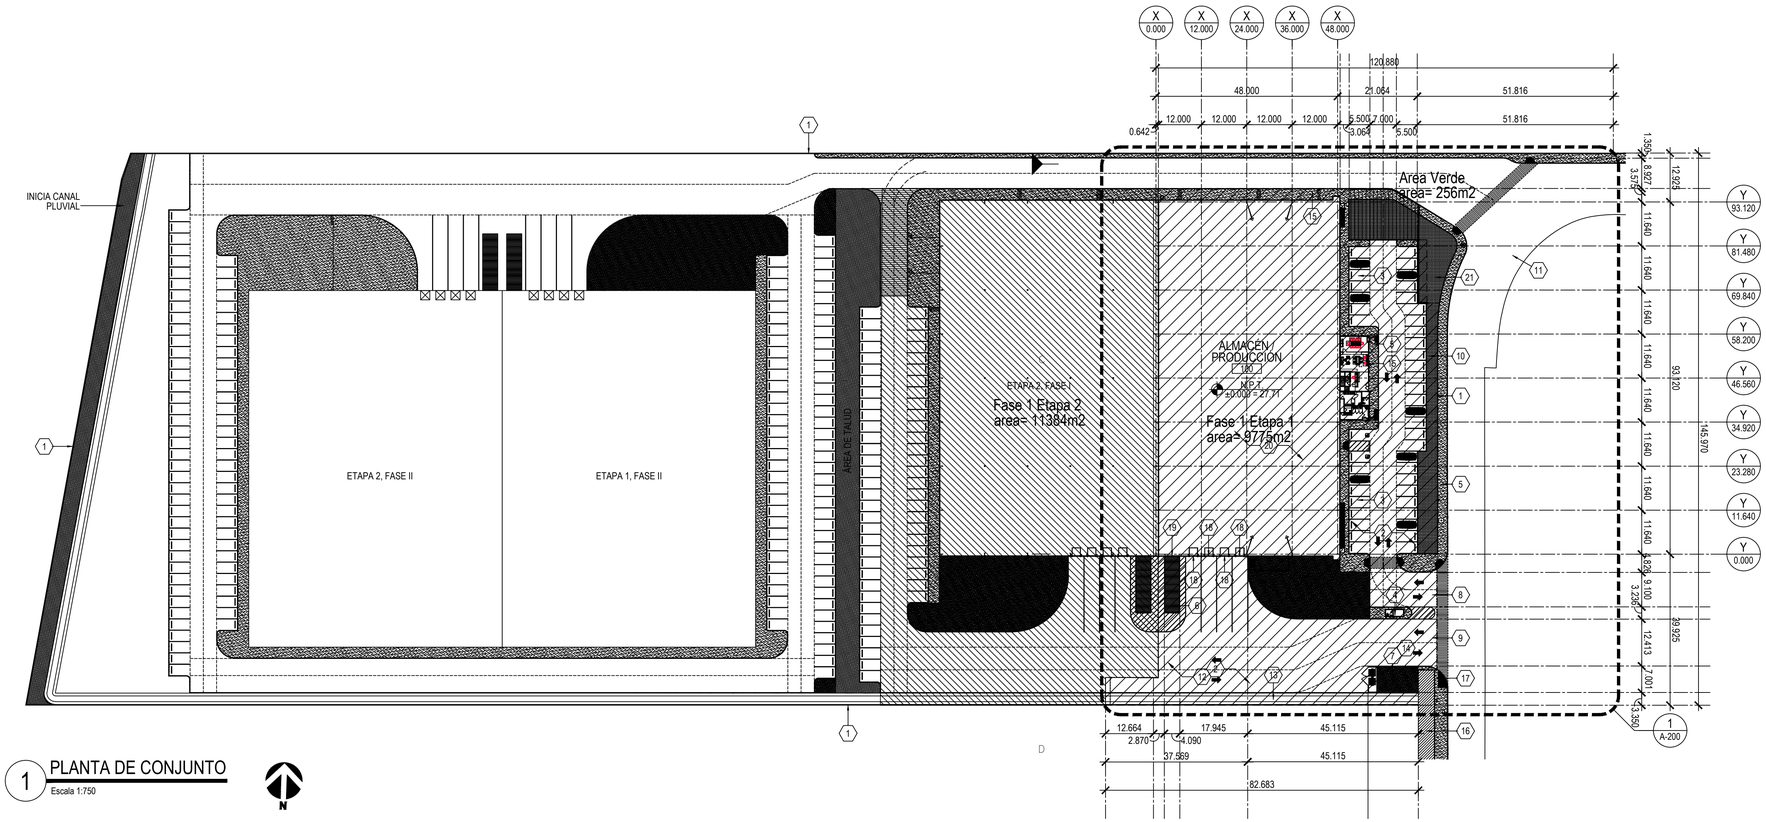

1 PLANTA DE CONJUNTO

Escala 1:750

N

SIMBOLOGÍA DEL SITIO

ESPACIO 000	INDICA NOMBRE Y ESPACIO
1 A-100	INDICA REFERENCIA DE DETALLE
Y 93.120	INDICA EJE
	INDICA POLÍGONO DE FASE I, ETAPA 1
	INDICA ÁREA DE GRAVA TRITURADA
	INDICA ÁREA DE BANQUETA
	INDICA ÁREA VERDE
	INDICA ÁREA DE FUTURO CRECIMIENTO.
	INDICA NIVEL

NOTAS ESPECÍFICAS

1. LÍMITE DE PROPIEDAD, VER MEDIDAS Y COORDENADAS EN DESLINDE CATASTRAL CERTIFICADO.
2. SUPERFICIE DE ASFALTO, VER PLANO DE PAVIMENTOS, ESTRUCTURA Y RASANTES; PARA NIVELES, DETALLES Y ESPECIFICACIONES.
3. CAJÓN DE ESTACIONAMIENTO TÍPICO (3.00 X 5.50 m)
4. CASETA DE VIGILANCIA, VER PLANO A-210.00.
5. ÁREA DE BANQUETA PEATONAL.
6. RAMPA PARA MONTACARGAS DE CONCRETO ARMADO Y ACABADO ESTRIADO.
7. ÁREA DE GRAVA TRITURADA DE 3/4" Ø.
8. ACCESO Y SALIDA DE AUTOMOVILES (TRÁFICO LIGERO)
9. ACCESO Y SALIDA DE TRACTOCAMIONES (TRÁFICO PESADO)
10. ÁREA VERDE.
11. CALLE EXISTENTE.
12. PATIO DE MANIOBRAS.
13. CANAL PLUVIAL, VER DETALLE -------
14. ÁREA DE EQUIPAMIENTO.
15. EDIFICIO DE OFICINAS, VER PLANO A-220.00.
16. CANAL PLUVIAL EXISTENTE.
17. BANCO DE NIVEL SOBRE POSTE ELÉCTRICO, CON COORDENADAS: X= 303,004.200, Y= 2436,914.935, Z= **1925.635.**
18. CORTINA METÁLICA DE 9' X 10', VER PLANO DE PUERTAS Y VENTANAS.
19. CORTINA METÁLICA DE 12' X 16', VER PLANO DE PUERTAS Y VENTANAS.
20. EL NIVEL DE PISO TERMINADO DE CONSTRUCCIÓN EN LA NAVE (**±0.000**) REPRESENTADO EN LOS PLANOS ARQUITECTÓNICOS ES EQUIVALENTE A LA ELEVACIÓN **1927.71** Ó **27.71** (VER PLANO DE PAVIMENTOS, ESTRUCTURA Y RASANTES).
21. INDICA ÁREA VERDE EN ÁREA DE USO COMÚN.

TABLA DE SUPERFICIES

DESCRIPCIÓN	UNIDAD
CARPETA ASFÁLTICA DE TRÁFICO LIGERO DE 5 cm	790.42 m^2
CARPETA ASFÁLTICA DE TRÁFICO PESADO DE 8 cm	1830.56 m^2
CARPETA ASFÁLTICA DE ESTACIONAMIENTO	781.70 m^2
SUPÉRFICIE DE BANQUETAS	710.00 m^2
CUBIERTA DE ALMACÉN	4650.00 m^2
CUBIERTA DE ENTREPISO (EDIFICIO DE OFICINAS)	150.00 m^2
CUBIERTA DE CASETA DE VIGILANCIA	10.25 m^2
CAJONES DE ESTACIONAMIENTO	44 CAJONES

LOCALIZACIÓN:

GRUPO NELSON

LIC. JUAN CARLOS NELSON LUKEN
PROPIETARIO Y/O REP. LEGAL

Bremer & Herrera
Architecture, Planning and Interiors

LAS IDEAS Y DISEÑOS REUNIDOS EN ESTE PLANO, INDICADOS Ó REPRESENTADOS POR MEDIO DE ESTE DIBUJO, SON PROPIEDAD DE ESPACIO BREMER HERRERA BREMER S. DE R.L. DE C.V. ESTOS FUERON CREADOS ÚNICAMENTE PARA USO PROPIO Y CON RELACIÓN AL PROYECTO. ESTOS PLANOS NO PODRÁN SER USADOS POR OTRAS PERSONAS O FIRMAS, AL MENOS QUE SEAN AUTORIZADOS POR ESPACIO BREMER HERRERA BREMER S. DE R.L. DE C.V. LOS CAMBIOS QUE SE HAGAN EN ELLOS DE DISEÑO Ó DIMENSIONES DEBERÁN SER ESPECIFICADOS EN PLANOS ESPECIALES.

REVISIÓN	SIMB.	DESCRIPCIÓN	FECHA

NOMBRE DE PROYECTO:

NAVE INDUSTRIAL, FASE I, ETAPA 1

TIPO DE PROYECTO:
NAVE INDUSTRIAL

UBICACIÓN:
CALLE 4 No. 500, INTERPUERTO PARQUE LOGÍSTICO FASE V AMPLIADA

PROPIETARIO: PROPIEDADES NELSON DE MEXICALI, S.A. DE C.V.

SUP. TERRRENO: 52,943.184 m^2 | SUP. CONST: 5,000.00 m^2

C.O.S: 4,825.00 m^2 (9.11%) | C.U.S: 5,000.00 m^2 (0.09)

CÁLCULO:
ING. BENJAMÍN TERÁN DURÁN

PERITO:
ARQ. ELSA CECILIA BREMER HERNÁNDEZ

CED. PROF. 129835 | REG. OP. 667 CED. PROF. 964383

PROYECTO:
BREMER & HERRERA ARQUITECTOS

DIBUJO:

NOMBRE DE PLANO:

FECHA:

ESCALA:

CLAVE:

CLAVE CATASTRAL:
2400102801000107340600007000000

ARCHIVO FUENTE: