N O T A :

EL PRESENTE DESLINDE SE REALIZO EN BASE A DATOS TOMADOS DE PLANO DE DESLINDE ANTERIOR, CERTIFICADO POR CATASTRO CON FECHA DE MARZO DEL 2023.

DATOS RPPC
FOLIO REAL: 418281
DE FECHA: 17 DE NOVIEMBRE DEL 2023
PARTIDA: 6001616

*LOTE: 7 FR. 4 P.6 F. B P.3 SEGUN R.P.P. Y C.

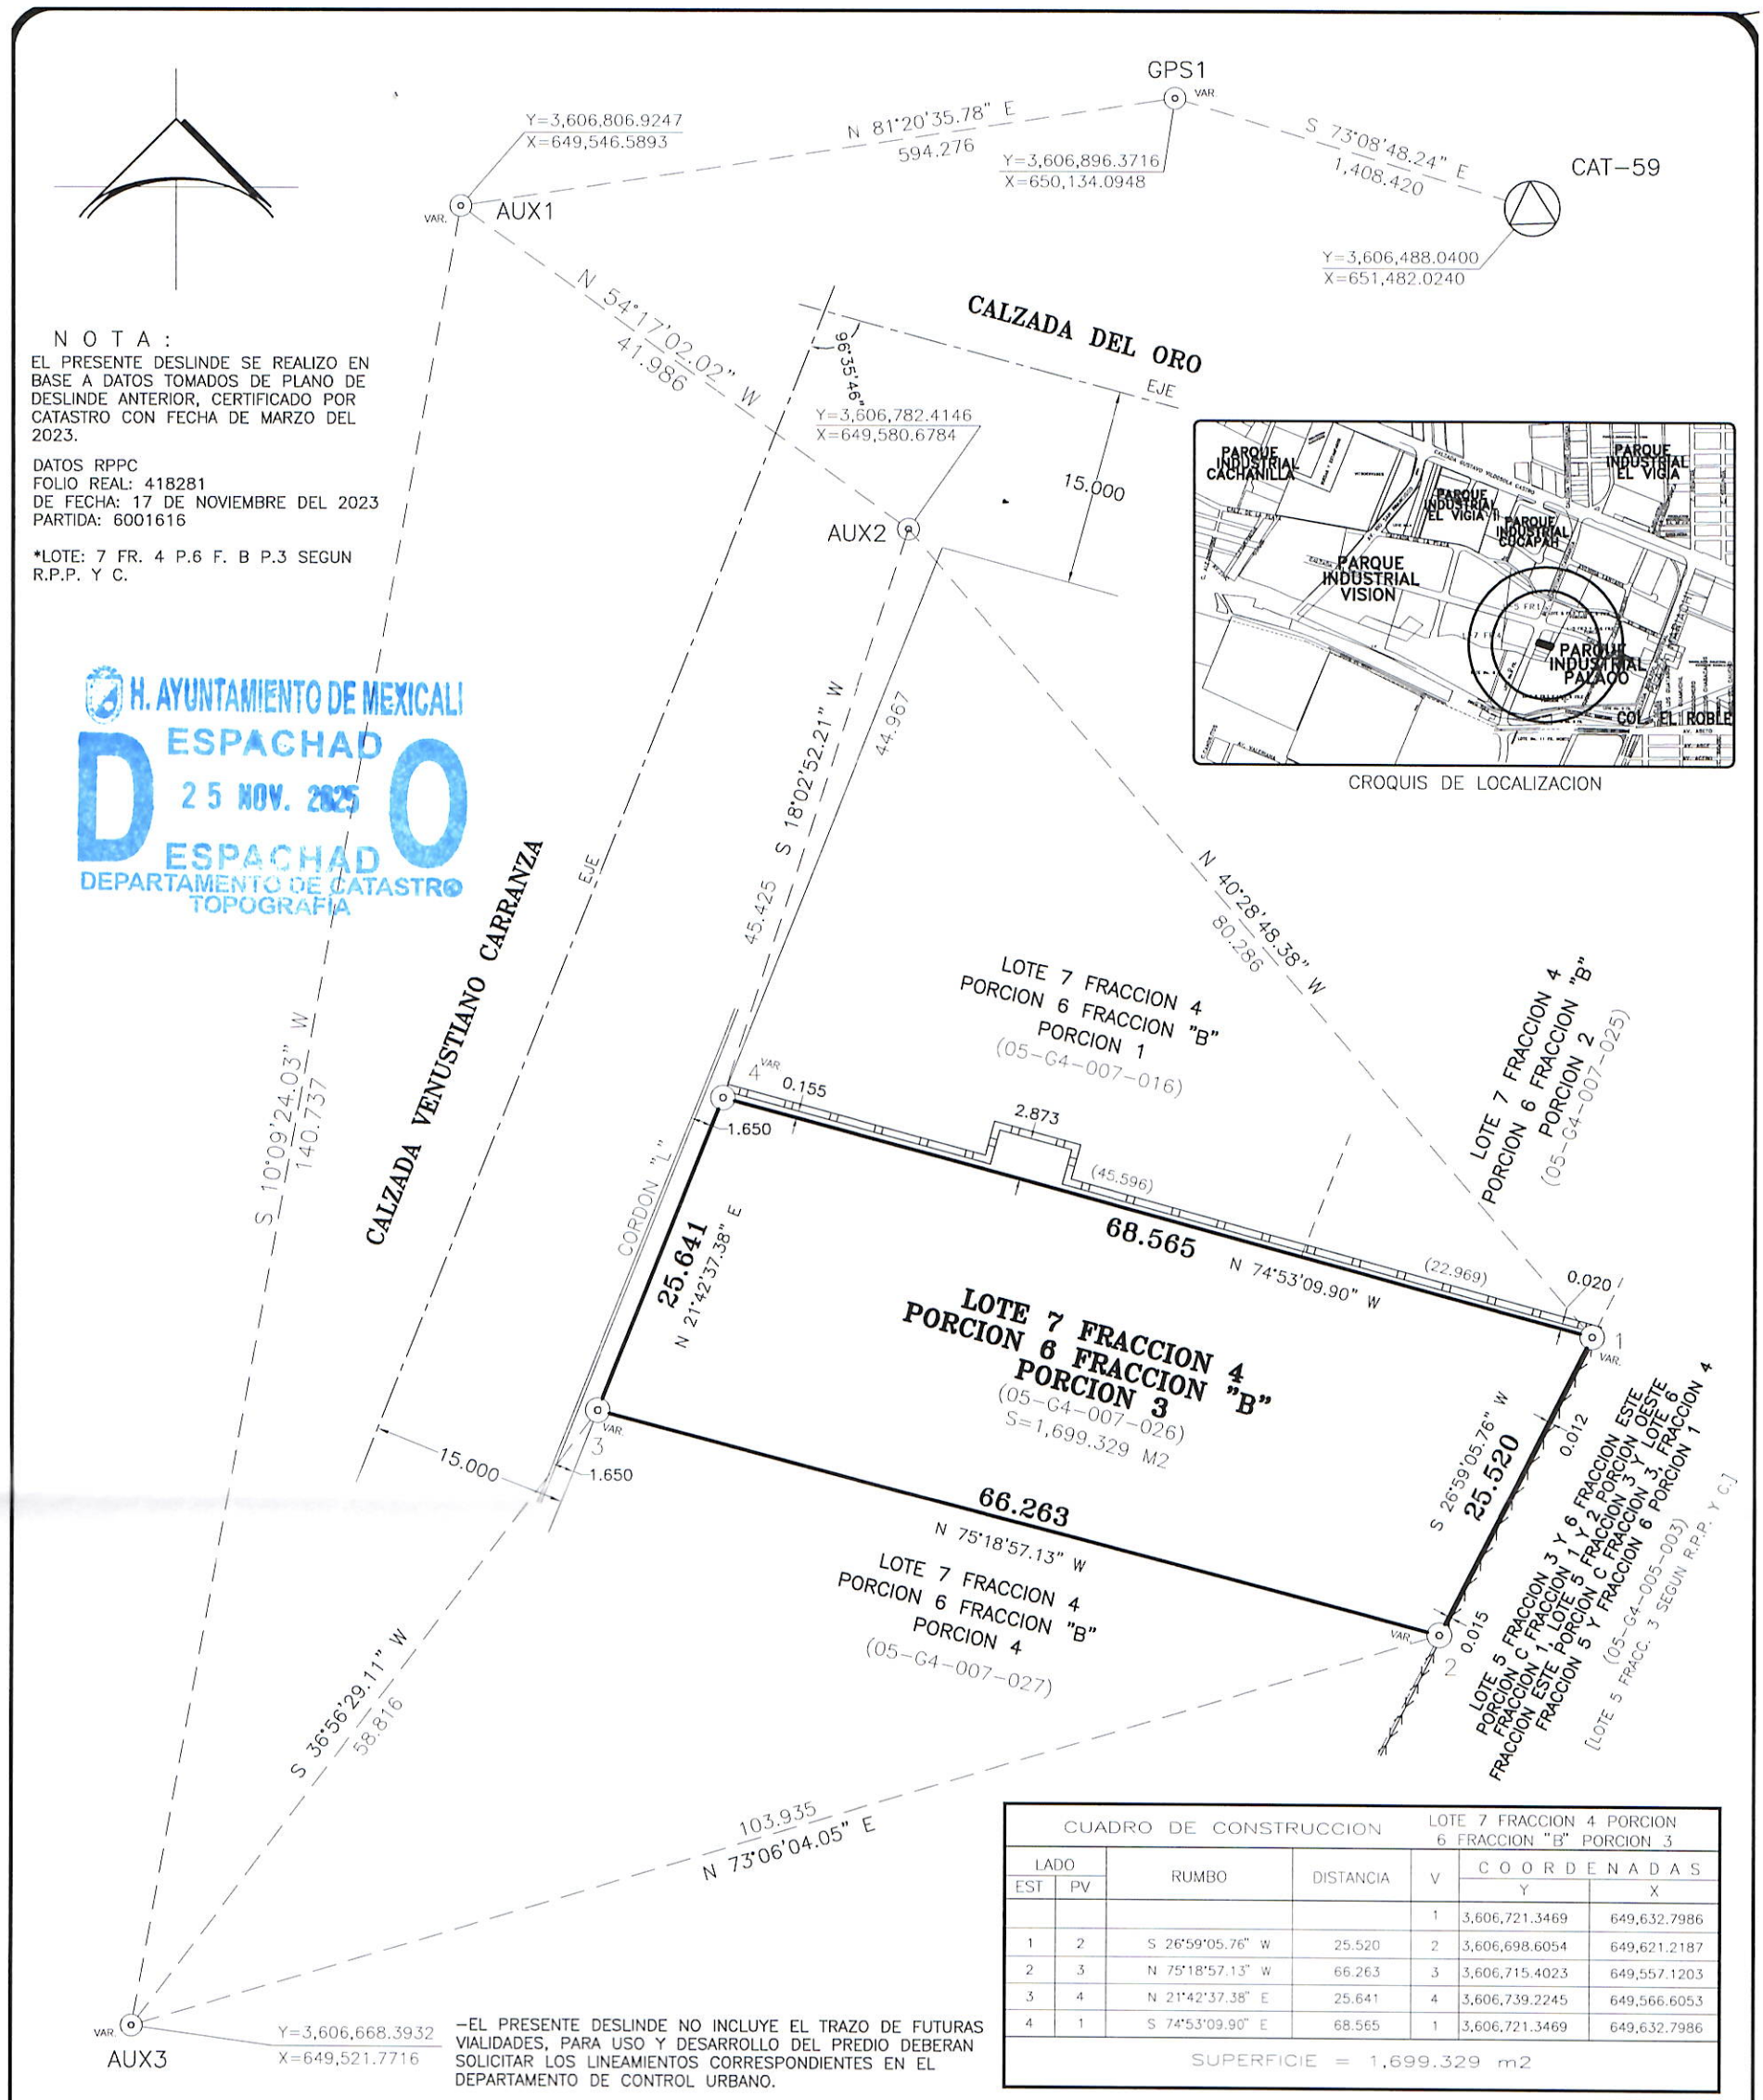

CROQUIS DE LOCALIZACION

H. AYUNTAMIENTO DE MEXICALI
DESPACHADO
25 NOV. 2025
DESPACHADO
DEPARTAMENTO DE CATASTRO
TOPOGRAFIA

-EL PRESENTE DESLINDE NO INCLUYE EL TRAZO DE FUTURAS VIALIDADES, PARA USO Y DESARROLLO DEL PREDIO DEBERAN SOLICITAR LOS LINEAMIENTOS CORRESPONDIENTES EN EL DEPARTAMENTO DE CONTROL URBANO.

CUADRO DE CONSTRUCCION				LOTE 7 FRACCION 4 PORCION 6 FRACCION "B" PORCION 3		
LADO		RUMBO	DISTANCIA	V	COORDENADAS	
EST	PV				Y	X
				1	3,606,721.3469	649,632.7986
1	2	S 26°59'05.76" W	25.520	2	3,606,698.6054	649,621.2187
2	3	N 75°18'57.13" W	66.263	3	3,606,715.4023	649,557.1203
3	4	N 21°42'37.38" E	25.641	4	3,606,739.2245	649,566.6053
4	1	S 74°53'09.90" E	68.565	1	3,606,721.3469	649,632.7986
SUPERFICIE = 1,699.329 m2						

ACTA DE DESLINDE

CLAVE CATASTRAL	LOTE	MANZANA	SUPERFICIE
05-G4-007-026	7 FRACCION 4 PORCION 6 FRACCION "B" PORCION 3	S/M	1,699.329 M2

EJIDO, POBLADO, COLONIA, DESARROLLO URBANO, FRACCIONAMIENTO	DELEGACION (SI APLICA)	LUGAR
2 DIVISION 2	CERRO PRIETO	MEXICALI B.C.

PROPIETARIO O POSEEDOR	SERVICIOS PUBLICOS
TAKIMYLDIZ, S.A. DE C.V.	A ☒ L ☒ D ☒ B ☒ C ☒ P ☒ T ☒ G ☐ AL ☒ CV ☒

PREDIO	USO ACTUAL DEL SUELO	FECHA DE ELABORACION	PLANO	ESCALA	ACOTACION
CONSTRUIDO ○ BALDIO ◎	INDUSTRIAL	31/OCTUBRE/2025	1/1	1: 125	METROS

EL DEPARTAMENTO DE CATASTRO MUNICIPAL DE MEXICALI

CERTIFICA

QUE EL PRESENTE DESLINDE CUMPLE CON LO ESTABLECIDO EN EL ARTICULO 44 DEL REGLAMENTO DEL CATASTRO INMOBILIARIO DEL MUNICIPIO DE MEXICALI Y ARTICULO XII DEL MANUAL TECNICO DE DESLINDES PARA EL MUNICIPIO DE MEXICALI, B. C. Y SALVO ERROR, OMISION O MODIFICACION, CORRESPONDEN A LOS DATOS QUE OBRAN EN ESTE DEPARTAMENTO DE CATASTRO BAJO CLAVE CATASTRAL INDICADA LOS CUALES FUERON VERIFICADOS Y REPLANTEADOS EN CAMPO POR EL PERITO FIRMANTE RESPONSABLE DE ESTOS TRABAJOS.

LOS DERECHOS FUERON PAGADOS CON EL RECIBO OFICIAL No. 92-7
DE FECHA: 7/11/25

EL C. COORDINADOR DEL AREA DE TOPOGRAFIA DEL DEPARTAMENTO DE CATASTRO DE LA DIRECCION DE ADMINISTRACION URBANA

ING. ADRIAN CERVANTES HUERTA

☐ PROPIETARIO ☐ POSEEDOR ☐ REPRESENTANTE LEGAL

PERITO RESPONSABLE No. 83

ING. CARLOS EDUARDO ARELLANO SOQUI
CEDULA ESTATAL 022054-01/14 CEDULA FEDERAL 8429031

REVISO ☐ TRAMITE NORMAL ☐ TRAMITE URGENTE