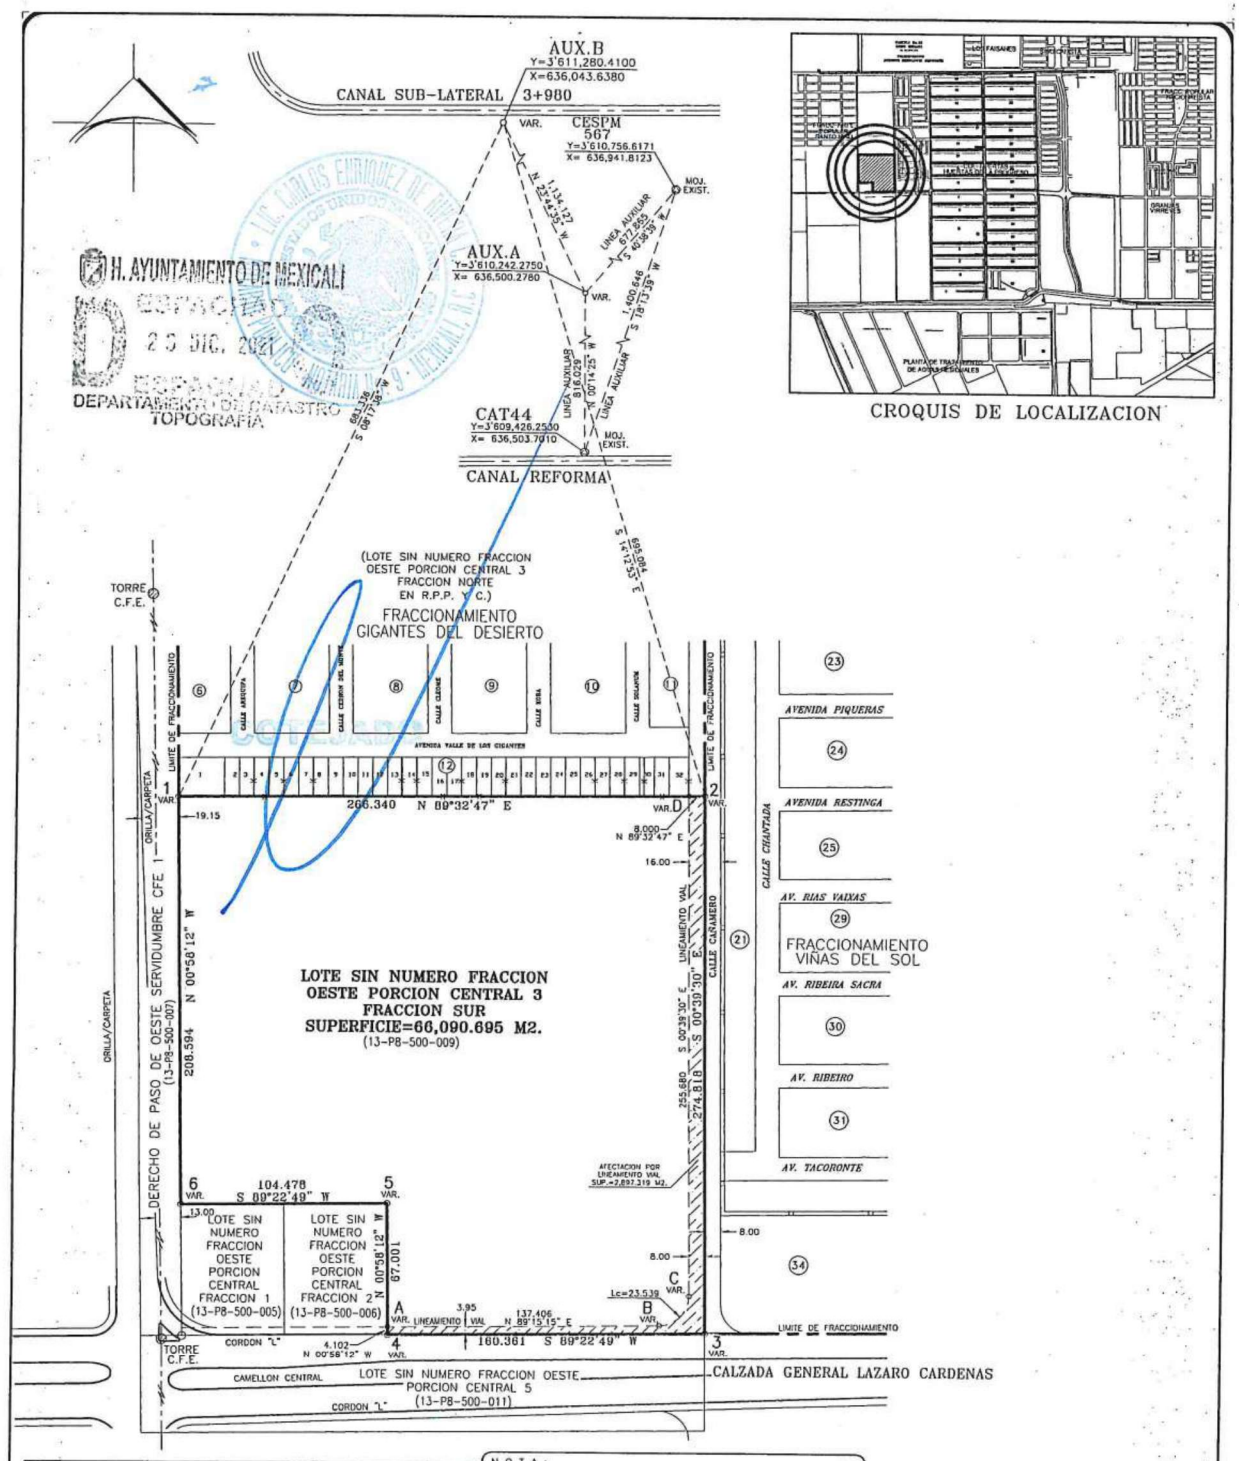

POLIGONO GENERAL

LADO EST	LADO PV	RUMBO	DISTANCIA	V	COORDENADAS Y	COORDENADAS X
				1	3,610,611.7196	635,946.1603
1	2	N 89°32'47" E	266.340	2	3,610,613.6287	636,212.4915
2	3	S 00°39'30" E	274.818	3	3,610,339.0288	636,215.6490
3	4	S 89°22'49" W	160.361	4	3,610,337.2940	636,055.2972
4	5	N 00°58'12" W	67.001	5	3,610,404.2857	636,054.1630
5	6	S 89°22'49" W	104.478	6	3,610,403.1554	635,949.6915
6	1	N 00°58'12" W	208.594	1	3,610,611.7196	635,946.1603

SUPERFICIE = 66,090.695 M2.

CUADRO DE CONSTRUCCION DE AFECTACION POR LINEAMIENTO VIAL

LADO EST	LADO PV	RUMBO	DISTANCIA	V	COORDENADAS Y	COORDENADAS X
				2	3,610,613.8287	636,212.4915
2	3	S 00°39'30" E	274.818	3	3,610,339.0288	636,215.6490
3	4	S 89°22'49" W	160.361	4	3,610,337.2940	636,055.2972
4	A	N 00°58'12" W	4.102	A	3,610,341.3955	636,055.2278
A	B	N 89°15'15" E	137.406	B	3,610,343.1842	636,192.6226
B	C	N 44°17'52" E CENTRO DE CURVA DELTA = 89°54'45" RADIO = 15.000	21.197 LONG. CURVA = 21.539 SUB.TAN.= 13.977	C CEN	3,610,358.3553 3,610,358.1829	636,207.4264 636,192.4274
C	D	N 00°39'30" W	255.427	D	3,610,613.7653	636,204.4917
D	2	N 89°32'47" E	8.000	2	3,610,613.8287	636,212.4915

SUPERFICIE = 2,897.319 M2.

NOTA:
EL PRESENTE DESLINDE SE REALIZO EN BASE A:

-LEVANTAMIENTO Y SUBDIVISION DEL LOTE SIN NUMERO FRACCION OESTE PORCION CENTRAL 3 CON CLAVE CATASTRAL 13-P8-500-009 DE FECHA 29 DE OCTUBRE DEL 2013.

ESTE TRABAJO SE LIGO AL VERTICE CAT44 ESTABLECIDOS POR CATASTRO MUNICIPAL EN SEPTIEMBRE DEL 2009 Y AL PUNTO DE CONTROL C-567 ESTABLECIDO POR CESPM EN COORDENADAS UTM DATUM WSG-84.

SUP. REGISTRADA = 66,090.695 M2.
SUPERCIE DE AFECTACION POR LINEAMIENTO VIAL = 2,897.319 M2.

* INSCRIPCION No. 5677065 SECCION CIVIL ANTE EL R.P.P. Y C. DE FECHA 04 DE NOVIEMBRE DE 2013, REFERENTE A SUBDIVISION DE PROPIEDAD. FOLIO REAL: 425363.

ACTA DE DESLINDE

CLAVE CATASTRAL: 13-P8-500-009	LOTE: SIN NUMERO FRACCION OESTE PORCION CENTRAL 3 FRACCION SUR	MANZANA: SIN MANZANA	SUPERFICIE: 66,090.695 M2.
COLONIA, POBLADO, FRACCIONAMIENTO O DESARROLLO URBANO: RANCHO CLIFFORD	DELEGACION (SI APLICA): PROGRESO		LUGAR: MEXICALI B.C.
PROPIETARIO O POSEEDOR: MERCEDES GRADILLA REGALADO DE CHAVEZ			SERVICIOS PUBLICOS: AGUA DRENAJE LUZ PAVIMENTO TELEFONO
PREDIO: CONSTRUIDO ○ BALDIO ●	USO ACTUAL DEL SUELO: RUSTICO	FECHA DE ELABORACION: 22 DE OCTUBRE DEL 2021	PLANO: 1/1 — ESCALA: 1: 2,500 — ACOTACION: METROS

EL DEPARTAMENTO DE CATASTRO MUNICIPAL DE MEXICALI

CERTIFICA

QUE EL PRESENTE DESLINDE CUMPLE CON LO ESTABLECIDO EN EL ARTICULO 44 DEL REGLAMENTO DEL CATASTRO INMOBILIARIO DEL MUNICIPIO DE MEXICALI Y ARTICULO XII DEL MANUAL TECNICO DE DESLINDES PARA EL MUNICIPIO DE MEXICALI, B. C., Y SALVO ERROR, OMISION O MODIFICACION, CORRESPONDE A LOS DATOS QUE OBRAN EN ESTE DEPARTAMENTO DE CATASTRO BAJO LA CLAVE CATASTRAL INDICADA LOS CUALES FUERON VERIFICADOS Y REPLANTEADOS EN CAMPO POR EL PERITO FIRMANTE RESPONSABLE DE ESTOS TRABAJOS.

LOS DERECHOS FUERON PAGADOS CON EL RECIBO OFICIAL NAMBRE DE FECHA 2/11/21

EL C. JEFE DEL DEPARTAMENTO

ARQ. LUIS FERNANDO CAMEZ MONTOYA

DIRECCIÓN DE TOPOGRAFIA

☐ PROPIETARIO ☐ POSEEDOR ☐ REPRESENTANTE LEGAL

PERITO RESPONSABLE No. 75

ING. ALEJANDRO PERA CARRILLO
CEDULA FEDERAL 6591668 RECORRIDO ESTATAL 023918-01/18
AV. ESPAÑA No. 2301 COL. URBANO ORIZABA
TEL.(686)557-40-00 E-MAIL servicios@ingpal.com

REVISO ☐ TRAMITE NORMAL ☐ TRAMITE URGENTE