DETALLE DE LIGA
FUERA DE ESCALA

CUADRO DE CONSTRUCCION DEL LOTE 18 FRACCION ESTE PORCION 3						
LADO		RUMBO	DISTANCIA	V	COORDENADAS	
EST	PV				Y	X
				1	3,610,773.5667	649,852.2140
1	2	S 00°35'52" E	98.564	2	3,610,675.0079	649,853.2425
2	3	S 89°19'06" W	77.107	3	3,610,674.0907	649,776.1405
3	1	N 37°24'24" E	125.230	1	3,610,773.5667	649,852.2140
SUPERFICIE = 3,800.000 M2.						

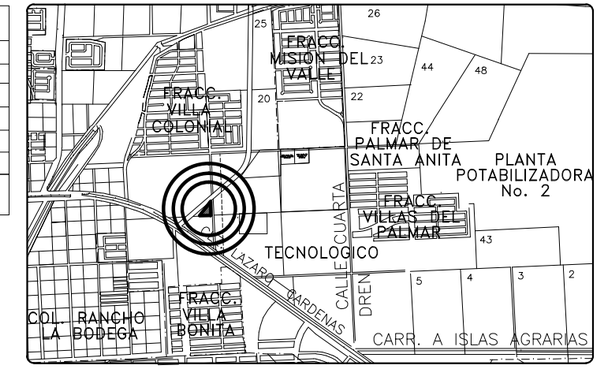

CROQUIS DE LOCALIZACION

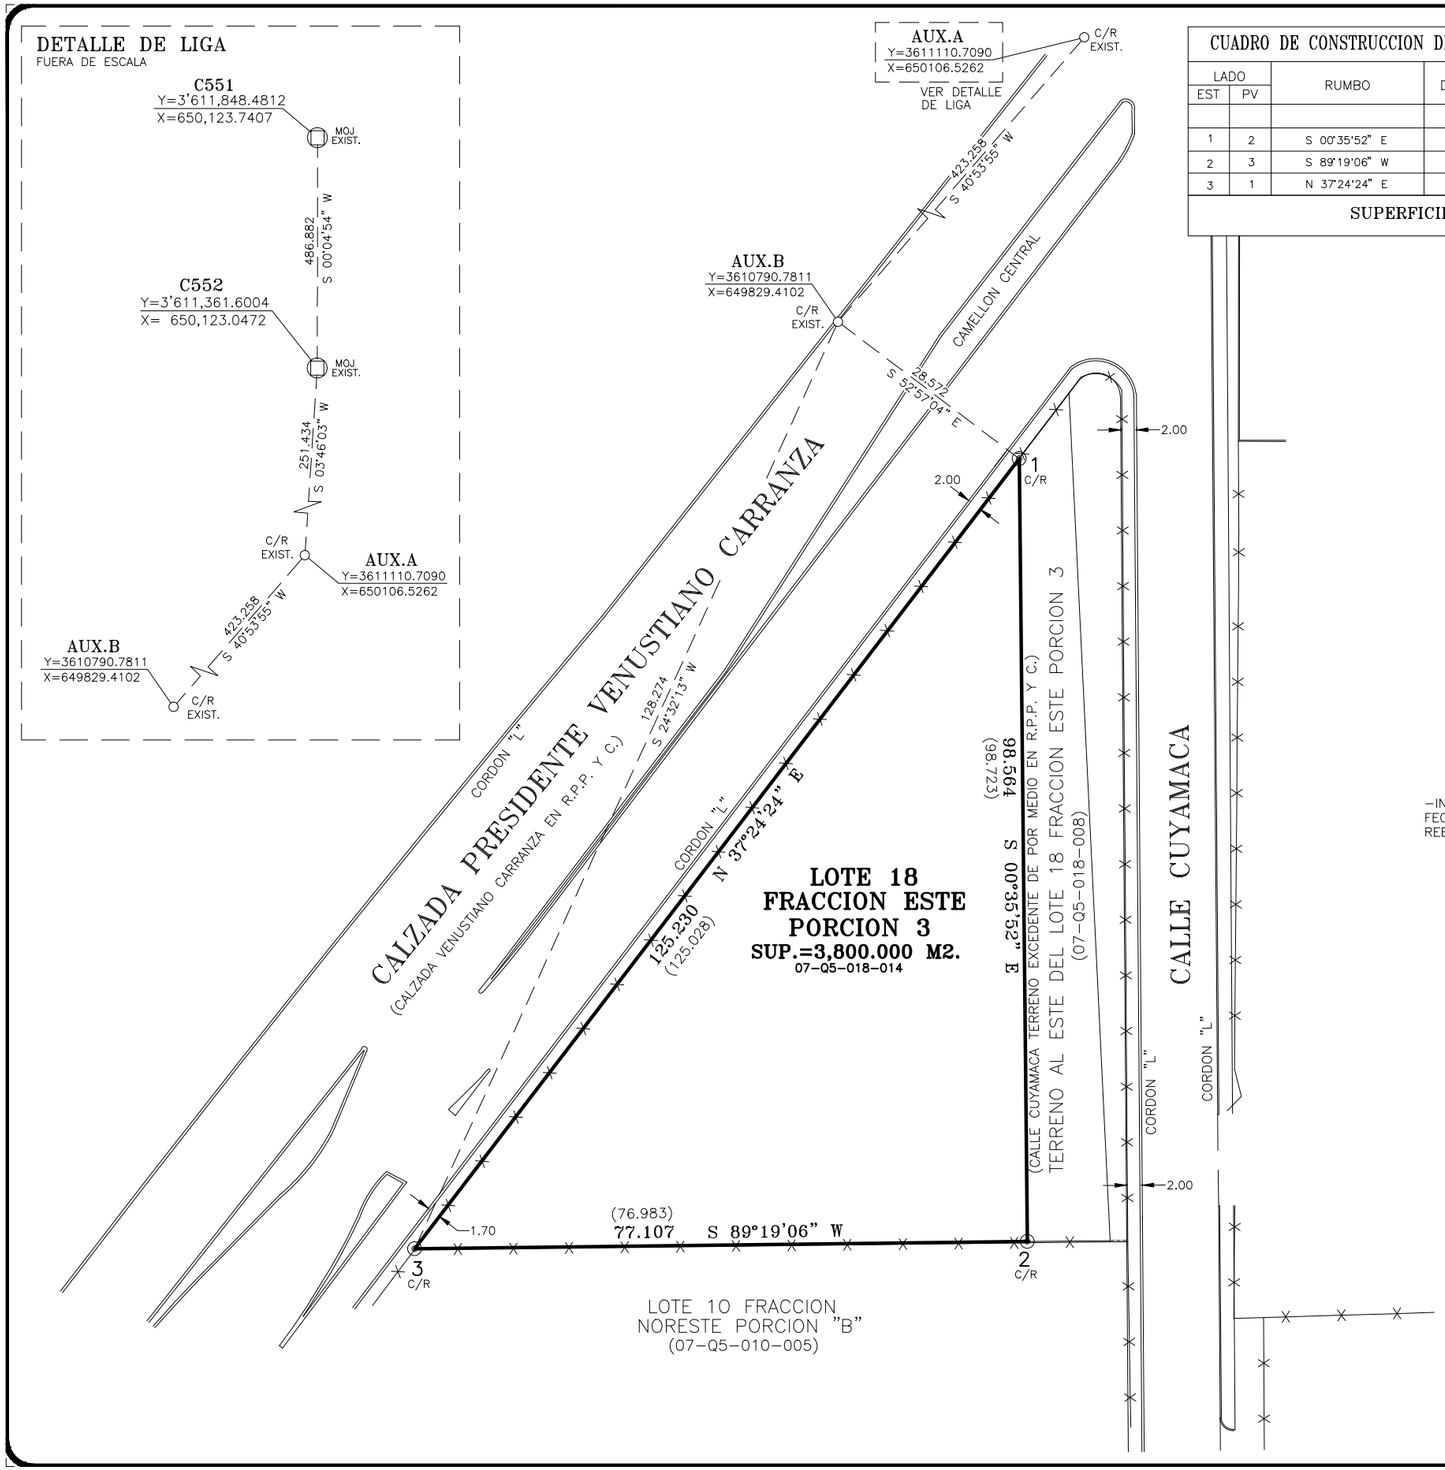

H.AYUNTAMIENTO DE MEXICALI
DESPACHADO
09/07/2021
DESPACHADO
DEPARTAMENTO DE CATASTRO
TOPOGRAFIA

(10.405) = DISTANCIA SEGUN R.P.P. Y C.
10.418 = DISTANCIA ANALITICA

-INSCRIPCION No.5460414 SECCION CIVIL ANTE EL R.P.P. Y C. DE FECHA 07 DE ENERO DEL 2008 REFERENTE A ESCRITURA EN REBELDIA, CON FOLIO REAL: 81445.

N O T A :
EL PRESENTE DESLINDE SE REALIZO EN BASE A:

-DESLINDE ANTERIOR DEL LOTE 18 FRACCION ESTE PORCION 3 CON CLAVE CATASTRAL 07-Q5-018-014 CERTIFICADO POR CATASTRO MUNICIPAL EL 17 DE NOVIEMBRE DEL 2015.

-DESLINDE ANTERIOR DEL TERRENO ESCEDENTE AL ESTE DEL LOTE 18 FRACCION ESTE PORCION 3 CON CLAVE CATASTRAL 07-Q5-018-008 CERTIFICADO POR CATASTRO MUNICIPAL EL 04 DE SEPTIEMBRE DEL 2008.

EL PRESENTE TRABAJO SE ENCUENTRA LIGADO POR LOS PUNTOS DE CONTROL C551 Y C552 ESTABLECIDOS POR CESPM, EN COORDENADAS UTM, DATUM WGS-84.

*COLONIA CALLES B.C. EN R.P.P. Y C.

ACTA DE DESLINDE

CLAVE CATASTRAL	MANZANA	LOTE	SUPERFICIE
07-Q5-018-014	SIN MANZANA	18 FRACCION ESTE PORCION 3	3,800.000 M2.
COLONIA, POBLADO, FRACCIONAMIENTO O DESARROLLO URBANO: CALLES		DELEGACION (SI APLICA): GONZALEZ ORTEGA	LUGAR: MEXICALI B.C.
PROPIETARIO O POSEEDOR: ROBERTO ARTURO MARQUEZ CARO			SERVICIOS PUBLICOS: A ☒ L ☒ D ☒ E ☒ C ☒ P ☒ T ☒ G ☐ AL ☒ CV ☐

PREDIO	USO ACTUAL DEL SUELO	FECHA DE ELABORACION	PLANO	ESCALA	ACOTACION
CONSTRUIDO ○ BALDIO ◍	COMERCIAL	11 DE JUNIO DEL 2021	1/1	1: 750	METROS

EL DEPARTAMENTO DE CATASTRO MUNICIPAL DE MEXICALI

CERTIFICA

QUE EL PRESENTE DESLINDE CUMPLE CON LO ESTABLECIDO EN EL ARTICULO 44 DEL REGLAMENTO DEL CATASTRO INMOBILIARIO DEL MUNICIPIO DE MEXICALI Y ARTICULO XII DEL MANUAL TECNICO DE DESLINDES PARA EL MUNICIPIO DE MEXICALI, B. C. Y SALVO ERROR, OMISION O MODIFICACION, LOS CUALES FUERON VERIFICADOS Y REPLANTEADOS EN CAMPO POR EL PERITO FIRMANTE RESPONSABLE DE ESTOS TRABAJOS.

EL PRESENTE DOCUMENTO SE EXPIDE CON FUNDAMENTO EN LOS ARTICULOS 10 Y 11 DEL REGLAMENTO DE FIRMA ELECTRONICA PARA EL GOBIERNO MUNICIPAL DE MEXICALI, BAJA CALIFORNIA.

EL C. JEFE DEL DEPARTAMENTO
DE CATASTRO

z9G0ImkDKwcQXjWxG2nh0dYhMTAme+
TQSCbbWNytT5Q=
PABLO PEÑA CARRILLO

ING. PABLO PEÑA CARRILLO

PERITO RESPONSABLE No.75

RdiHGaPSFVMnahHjuWwTq6Qn22WG8o
NZR9GrbfIEBoE=
ALEJANDRO PEÑA CARRILLO

ING. ALEJANDRO PEÑA CARRILLO
CEDULA FEDERAL 6691668 REGISTRO ESTATAL 025926-01/19
AV. ESPAÑA No. 2301 CONJ. URBANO ORIZABA
TEL.(686)557-40-00 E-MAIL servicios@topgral.com